


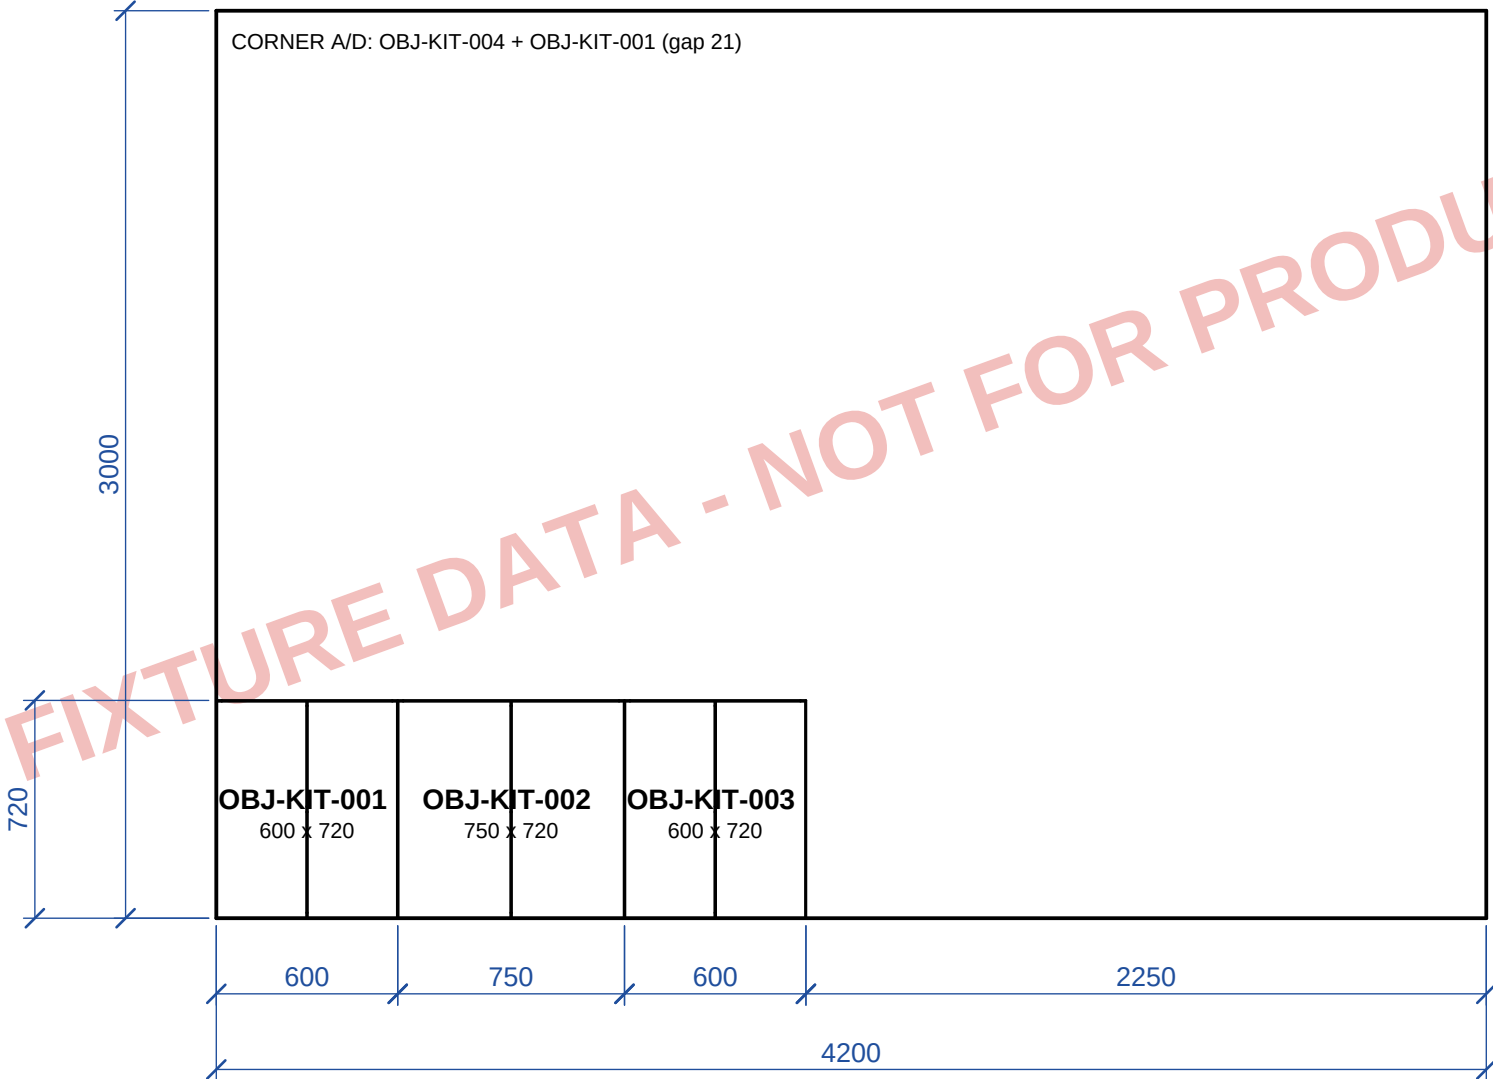


WALL A INTERNAL ELEVATION KITCHEN SCALE 1:25

NOTES

1. All dimensions in millimetres. Dimensions are read from the resolved room model, not measured from this drawing.
2. View from inside the room facing wall A; visible edges only. Objects on other walls are shown on their own wall elevations.
3. RUN:A:1: OBJ-KIT-001, OBJ-KIT-002, OBJ-KIT-003 (length 1950).
4. Adjacency: OBJ-KIT-001/OBJ-KIT-002 touching; OBJ-KIT-002/OBJ-KIT-003 touching.
5. Corner D/A: OBJ-KIT-004 + OBJ-KIT-001, gap 21.
6. Derived from design version dv\_001; planning standard TEST\_FIXTURE\_PLANNING\_STANDARD v0.0.1 (TEST\_FIXTURE); 4 object(s).
7. TEST FIXTURE data in use: construction standard TEST\_FIXTURE\_CONSTRUCTION\_STANDARD; hardware dataset HETTICH\_TEST\_FIXTURE; planning standard TEST\_FIXTURE\_PLANNING\_STANDARD. Values are synthetic.
8. 30 validation BLOCKER(s) outstanding: this drawing must not be used for production.

|                       |                                     |
|-----------------------|-------------------------------------|
| PROJECT               | LSA-BLR-2026-0001 (project_001)     |
| ROOM                  | Kitchen                             |
| DRAWING TITLE         | WALL A INTERNAL ELEVATION - KITCHEN |
| DRAWING NO. / SHEET   | KIT-WE-A SHEET 1 OF 1               |
| REVISION / DATE       | A 2026-09-26                        |
| DESIGNER / CHECKER    | TEST DESIGNER / UNASSIGNED          |
| SCALE                 | 1:25                                |
| APPROVAL STATUS       | PRELIMINARY                         |
| SOURCE DESIGN VERSION | dv_001 (DRAFT)                      |
| MODEL FINGERPRINT     | 0ae96d596b740a                      |
| DATA CLASSIFICATION   | TEST_FIXTURE                        |

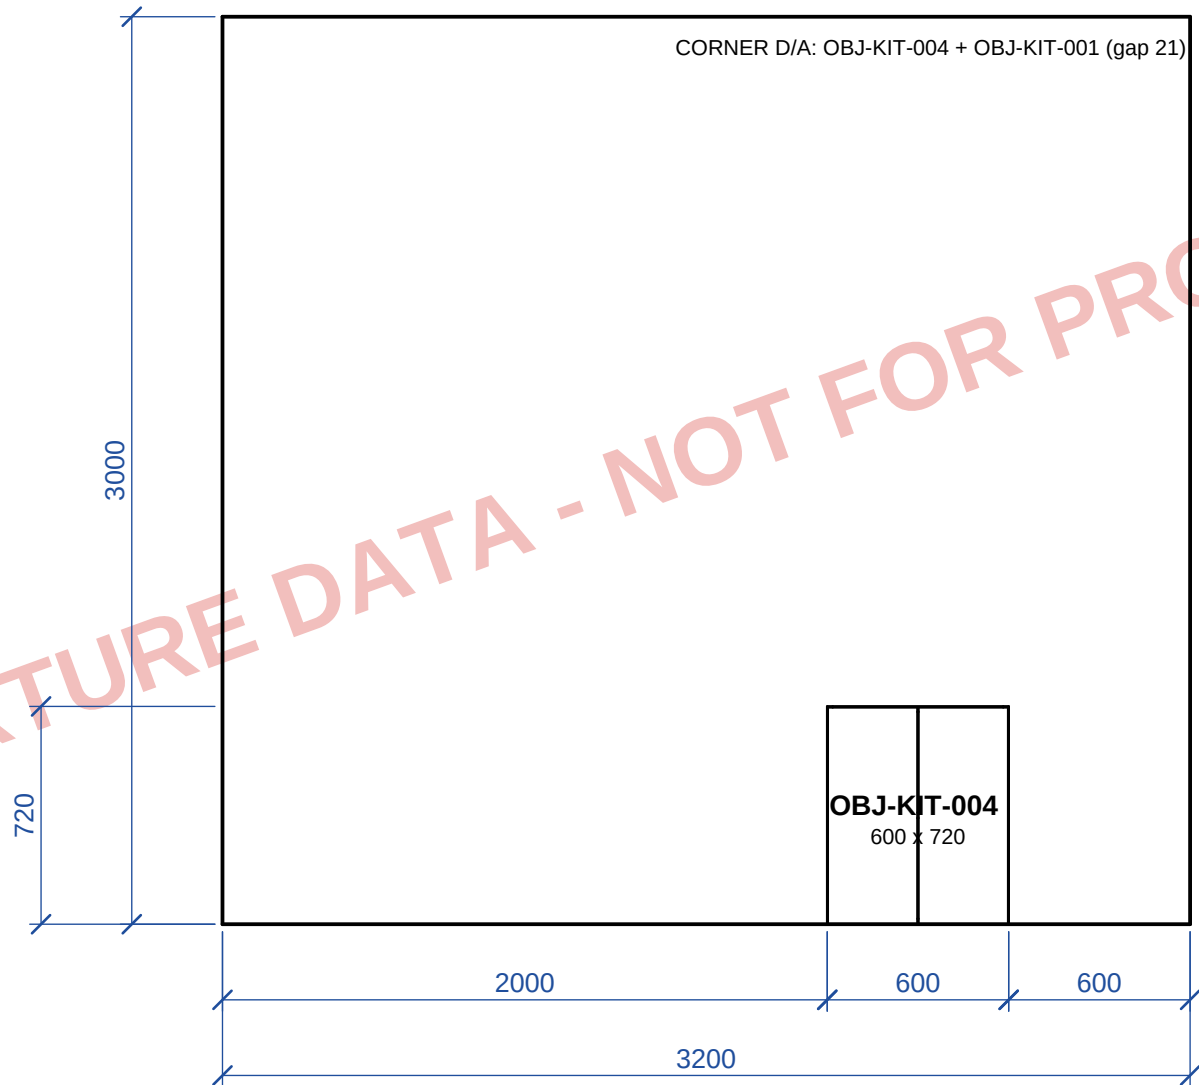

WALL D INTERNAL ELEVATION KITCHEN SCALE 1:25

NOTES

1. All dimensions in millimetres. Dimensions are read from the resolved room model, not measured from this drawing.
2. View from inside the room facing wall D; visible edges only. Objects on other walls are shown on their own wall elevations.
3. RUN:D:1: OBJ-KIT-004 (length 600).
4. Corner D/A: OBJ-KIT-004 + OBJ-KIT-001, gap 21.
5. Derived from design version dv\_001; planning standard TEST\_FIXTURE\_PLANNING\_STANDARD v0.0.1 (TEST\_FIXTURE); 4 object(s).
6. TEST FIXTURE data in use: construction standard TEST\_FIXTURE\_CONSTRUCTION\_STANDARD; hardware dataset HETTICH\_TEST\_FIXTURE; planning standard TEST\_FIXTURE\_PLANNING\_STANDARD. Values are synthetic.
7. 30 validation BLOCKER(s) outstanding: this drawing must not be used for production.

|                       |                                     |
|-----------------------|-------------------------------------|
| PROJECT               | LSA-BLR-2026-0001 (project_001)     |
| ROOM                  | Kitchen                             |
| DRAWING TITLE         | WALL D INTERNAL ELEVATION - KITCHEN |
| DRAWING NO. / SHEET   | KIT-WE-D SHEET 1 OF 1               |
| REVISION / DATE       | A 2026-09-26                        |
| DESIGNER / CHECKER    | TEST DESIGNER / UNASSIGNED          |
| SCALE                 | 1:25                                |
| APPROVAL STATUS       | PRELIMINARY                         |
| SOURCE DESIGN VERSION | dv_001 (DRAFT)                      |
| MODEL FINGERPRINT     | 0ae96d596b740a                      |
| DATA CLASSIFICATION   | TEST_FIXTURE                        |

ROOM PANEL SCHEDULE KITCHEN

| NO | COMPONENT ID       | TYPE              | W   | H   | T   | MATERIAL       | GRAIN  | EDGE BANDING            | FINISH            | QTY | STATUS    |
|----|--------------------|-------------------|-----|-----|-----|----------------|--------|-------------------------|-------------------|-----|-----------|
|    | OBJ-KIT-001        | KIT_BASE_STANDARD | 600 | 720 | 560 |                |        | WALL A @ 0              |                   |     | OBJECT    |
| 1  | OBJ-KIT-001-SL     | SIDE_LEFT         | 560 | 720 | 18  | BOARD_BWP_18   | HEIGHT | EDGE_ABS_0_8MM (F)      | -                 | 1   | GENERATED |
| 2  | OBJ-KIT-001-SR     | SIDE_RIGHT        | 560 | 720 | 18  | BOARD_BWP_18   | HEIGHT | EDGE_ABS_0_8MM (F)      | -                 | 1   | GENERATED |
| 3  | OBJ-KIT-001-BOT    | BOTTOM            | 564 | 560 | 18  | BOARD_BWP_18   | WIDTH  | EDGE_ABS_0_8MM (F)      | -                 | 1   | GENERATED |
| 4  | OBJ-KIT-001-TSF    | TOP_SUPPORT_FRONT | 564 | 100 | 18  | BOARD_BWP_18   | WIDTH  | EDGE_ABS_0_8MM (F)      | -                 | 1   | GENERATED |
| 5  | OBJ-KIT-001-TSB    | TOP_SUPPORT_BACK  | 564 | 100 | 18  | BOARD_BWP_18   | WIDTH  | NONE                    | -                 | 1   | GENERATED |
| 6  | OBJ-KIT-001-BCK    | BACK              | 580 | 710 | 6   | BOARD_BACK_6   | NONE   | NONE                    | -                 | 1   | GENERATED |
| 7  | OBJ-KIT-001-SHF-01 | SHELF             | 562 | 518 | 18  | BOARD_BWP_18   | WIDTH  | EDGE_ABS_0_8MM (F)      |                   | 1   | GENERATED |
| 8  | OBJ-KIT-001-SHT-L  | SHUTTER           | 297 | 717 | 18  | BOARD_HDHMR_18 | HEIGHT | EDGE_ABS_2MM (T/BT/L/R) | LAMINATE_WHITE x2 | 1   | GENERATED |
| 9  | OBJ-KIT-001-SHT-R  | SHUTTER           | 297 | 717 | 18  | BOARD_HDHMR_18 | HEIGHT | EDGE_ABS_2MM (T/BT/L/R) | LAMINATE_WHITE x2 | 1   | GENERATED |
|    | OBJ-KIT-002        | KIT_BASE_STANDARD | 750 | 720 | 560 |                |        | WALL A @ 600            |                   |     | OBJECT    |
| 10 | OBJ-KIT-002-SL     | SIDE_LEFT         | 560 | 720 | 18  | BOARD_BWP_18   | HEIGHT | EDGE_ABS_0_8MM (F)      | -                 | 1   | GENERATED |
| 11 | OBJ-KIT-002-SR     | SIDE_RIGHT        | 560 | 720 | 18  | BOARD_BWP_18   | HEIGHT | EDGE_ABS_0_8MM (F)      | -                 | 1   | GENERATED |
| 12 | OBJ-KIT-002-BOT    | BOTTOM            | 714 | 560 | 18  | BOARD_BWP_18   | WIDTH  | EDGE_ABS_0_8MM (F)      | -                 | 1   | GENERATED |
| 13 | OBJ-KIT-002-TSF    | TOP_SUPPORT_FRONT | 714 | 100 | 18  | BOARD_BWP_18   | WIDTH  | EDGE_ABS_0_8MM (F)      | -                 | 1   | GENERATED |
| 14 | OBJ-KIT-002-TSB    | TOP_SUPPORT_BACK  | 714 | 100 | 18  | BOARD_BWP_18   | WIDTH  | NONE                    | -                 | 1   | GENERATED |
| 15 | OBJ-KIT-002-BCK    | BACK              | 730 | 710 | 6   | BOARD_BACK_6   | NONE   | NONE                    | -                 | 1   | GENERATED |
| 16 | OBJ-KIT-002-SHF-01 | SHELF             | 712 | 518 | 18  | BOARD_BWP_18   | WIDTH  | EDGE_ABS_0_8MM (F)      | -                 | 1   | GENERATED |
| 17 | OBJ-KIT-002-SHT-L  | SHUTTER           | 372 | 717 | 18  | BOARD_HDHMR_18 | HEIGHT | EDGE_ABS_2MM (T/BT/L/R) | LAMINATE_WHITE x2 | 1   | GENERATED |
| 18 | OBJ-KIT-002-SHT-R  | SHUTTER           | 372 | 717 | 18  | BOARD_HDHMR_18 | HEIGHT | EDGE_ABS_2MM (T/BT/L/R) | LAMINATE_WHITE x2 | 1   | GENERATED |
|    | OBJ-KIT-003        | KIT_BASE_STANDARD | 600 | 720 | 560 |                |        | WALL A @ 1350           |                   |     | OBJECT    |
| 19 | OBJ-KIT-003-SL     | SIDE_LEFT         | 560 | 720 | 18  | BOARD_BWP_18   | HEIGHT | EDGE_ABS_0_8MM (F)      | -                 | 1   | GENERATED |
| 20 | OBJ-KIT-003-SR     | SIDE_RIGHT        | 560 | 720 | 18  | BOARD_BWP_18   | HEIGHT | EDGE_ABS_0_8MM (F)      | -                 | 1   | GENERATED |
| 21 | OBJ-KIT-003-BOT    | BOTTOM            | 564 | 560 | 18  | BOARD_BWP_18   | WIDTH  | EDGE_ABS_0_8MM (F)      | -                 | 1   | GENERATED |
| 22 | OBJ-KIT-003-TSF    | TOP_SUPPORT_FRONT | 564 | 100 | 18  | BOARD_BWP_18   | WIDTH  | EDGE_ABS_0_8MM (F)      | -                 | 1   | GENERATED |
| 23 | OBJ-KIT-003-TSB    | TOP_SUPPORT_BACK  | 564 | 100 | 18  | BOARD_BWP_18   | WIDTH  | NONE                    | -                 | 1   | GENERATED |

NOTES

1. All dimensions in millimetres. Dimensions are read from the resolved room model, not measured from this drawing.
2. Edge codes: F front, BK back, T top, BT bottom, L left, R right. Rows grouped by object.
3. Derived from design version dv\_001; planning standard TEST\_FIXTURE\_PLANNING\_STANDARD v0.0.1 (TEST\_FIXTURE); 4 object(s).
4. TEST FIXTURE data in use: construction standard TEST\_FIXTURE\_CONSTRUCTION\_STANDARD; hardware dataset HETTICH\_TEST\_FIXTURE; planning standard TEST\_FIXTURE\_PLANNING\_STANDARD. Values are synthetic.
5. 30 validation BLOCKER(s) outstanding: this drawing must not be used for production.

|                       |                                 |
|-----------------------|---------------------------------|
| PROJECT               | LSA-BLR-2026-0001 (project_001) |
| ROOM                  | Kitchen                         |
| DRAWING TITLE         | ROOM PANEL SCHEDULE - KITCHEN   |
| DRAWING NO. / SHEET   | KIT-RPS-001 SHEET 1 OF 2        |
| REVISION / DATE       | A 2026-09-26                    |
| DESIGNER / CHECKER    | TEST DESIGNER / UNASSIGNED      |
| SCALE                 | NTS                             |
| APPROVAL STATUS       | PRELIMINARY                     |
| SOURCE DESIGN VERSION | dv_001 (DRAFT)                  |
| MODEL FINGERPRINT     | 0ae96d596b740a                  |
| DATA CLASSIFICATION   | TEST_FIXTURE                    |

ROOM PANEL SCHEDULE KITCHEN

| NO | COMPONENT ID       | TYPE              | W   | H   | T   | MATERIAL       | GRAIN  | EDGE BANDING            | FINISH            | QTY | STATUS    |
|----|--------------------|-------------------|-----|-----|-----|----------------|--------|-------------------------|-------------------|-----|-----------|
| 24 | OBJ-KIT-003-BCK    | BACK              | 580 | 710 | 6   | BOARD_BACK_6   | NONE   | NONE                    | -                 | 1   | GENERATED |
| 25 | OBJ-KIT-003-SHF-01 | SHELF             | 562 | 518 | 18  | BOARD_BWP_18   | WIDTH  | EDGE_ABS_0_8MM (F)      | -                 | 1   | GENERATED |
| 26 | OBJ-KIT-003-SHT-L  | SHUTTER           | 297 | 717 | 18  | BOARD_HDHMR_18 | HEIGHT | EDGE_ABS_2MM (T/BT/L/R) | LAMINATE_WHITE x2 | 1   | GENERATED |
| 27 | OBJ-KIT-003-SHT-R  | SHUTTER           | 297 | 717 | 18  | BOARD_HDHMR_18 | HEIGHT | EDGE_ABS_2MM (T/BT/L/R) | LAMINATE_WHITE x2 | 1   | GENERATED |
|    | OBJ-KIT-004        | KIT_BASE_STANDARD | 600 | 720 | 560 |                |        | WALL D @ 2000           |                   |     | OBJECT    |
| 28 | OBJ-KIT-004-SL     | SIDE_LEFT         | 560 | 720 | 18  | BOARD_BWP_18   | HEIGHT | EDGE_ABS_0_8MM (F)      | -                 | 1   | GENERATED |
| 29 | OBJ-KIT-004-SR     | SIDE_RIGHT        | 560 | 720 | 18  | BOARD_BWP_18   | HEIGHT | EDGE_ABS_0_8MM (F)      | -                 | 1   | GENERATED |
| 30 | OBJ-KIT-004-BOT    | BOTTOM            | 564 | 560 | 18  | BOARD_BWP_18   | WIDTH  | EDGE_ABS_0_8MM (F)      |                   | 1   | GENERATED |
| 31 | OBJ-KIT-004-TSF    | TOP_SUPPORT_FRONT | 564 | 100 | 18  | BOARD_BWP_18   | WIDTH  | EDGE_ABS_0_8MM (F)      |                   | 1   | GENERATED |
| 32 | OBJ-KIT-004-TSB    | TOP_SUPPORT_BACK  | 564 | 100 | 18  | BOARD_BWP_18   | WIDTH  | NONE                    | -                 | 1   | GENERATED |
| 33 | OBJ-KIT-004-BCK    | BACK              | 580 | 710 | 6   | BOARD_BACK_6   | NONE   | NONE                    | -                 | 1   | GENERATED |
| 34 | OBJ-KIT-004-SHF-01 | SHELF             | 562 | 518 | 18  | BOARD_BWP_18   | WIDTH  | EDGE_ABS_0_8MM (F)      | -                 | 1   | GENERATED |
| 35 | OBJ-KIT-004-SHT-L  | SHUTTER           | 297 | 717 | 18  | BOARD_HDHMR_18 | HEIGHT | EDGE_ABS_2MM (T/BT/L/R) | LAMINATE_WHITE x2 | 1   | GENERATED |
| 36 | OBJ-KIT-004-SHT-R  | SHUTTER           | 297 | 717 | 18  | BOARD_HDHMR_18 | HEIGHT | EDGE_ABS_2MM (T/BT/L/R) | LAMINATE_WHITE x2 | 1   | GENERATED |

NOTES

1. All dimensions in millimetres. Dimensions are read from the resolved room model, not measured from this drawing.
2. Edge codes: F front, BK back, T top, BT bottom, L left, R right. Rows grouped by object.
3. Derived from design version dv\_001; planning standard TEST\_FIXTURE\_PLANNING\_STANDARD v0.0.1 (TEST\_FIXTURE); 4 object(s).
4. TEST FIXTURE data in use: construction standard TEST\_FIXTURE\_CONSTRUCTION\_STANDARD; hardware dataset HETTICH\_TEST\_FIXTURE; planning standard TEST\_FIXTURE\_PLANNING\_STANDARD. Values are synthetic.
5. 30 validation BLOCKER(s) outstanding: this drawing must not be used for production.

|                       |                                 |
|-----------------------|---------------------------------|
| PROJECT               | LSA-BLR-2026-0001 (project_001) |
| ROOM                  | Kitchen                         |
| DRAWING TITLE         | ROOM PANEL SCHEDULE - KITCHEN   |
| DRAWING NO. / SHEET   | KIT-RPS-001 SHEET 2 OF 2        |
| REVISION / DATE       | A 2026-09-26                    |
| DESIGNER / CHECKER    | TEST DESIGNER / UNASSIGNED      |
| SCALE                 | NTS                             |
| APPROVAL STATUS       | PRELIMINARY                     |
| SOURCE DESIGN VERSION | dv_001 (DRAFT)                  |
| MODEL FINGERPRINT     | 0ae96d596b740a                  |
| DATA CLASSIFICATION   | TEST_FIXTURE                    |