


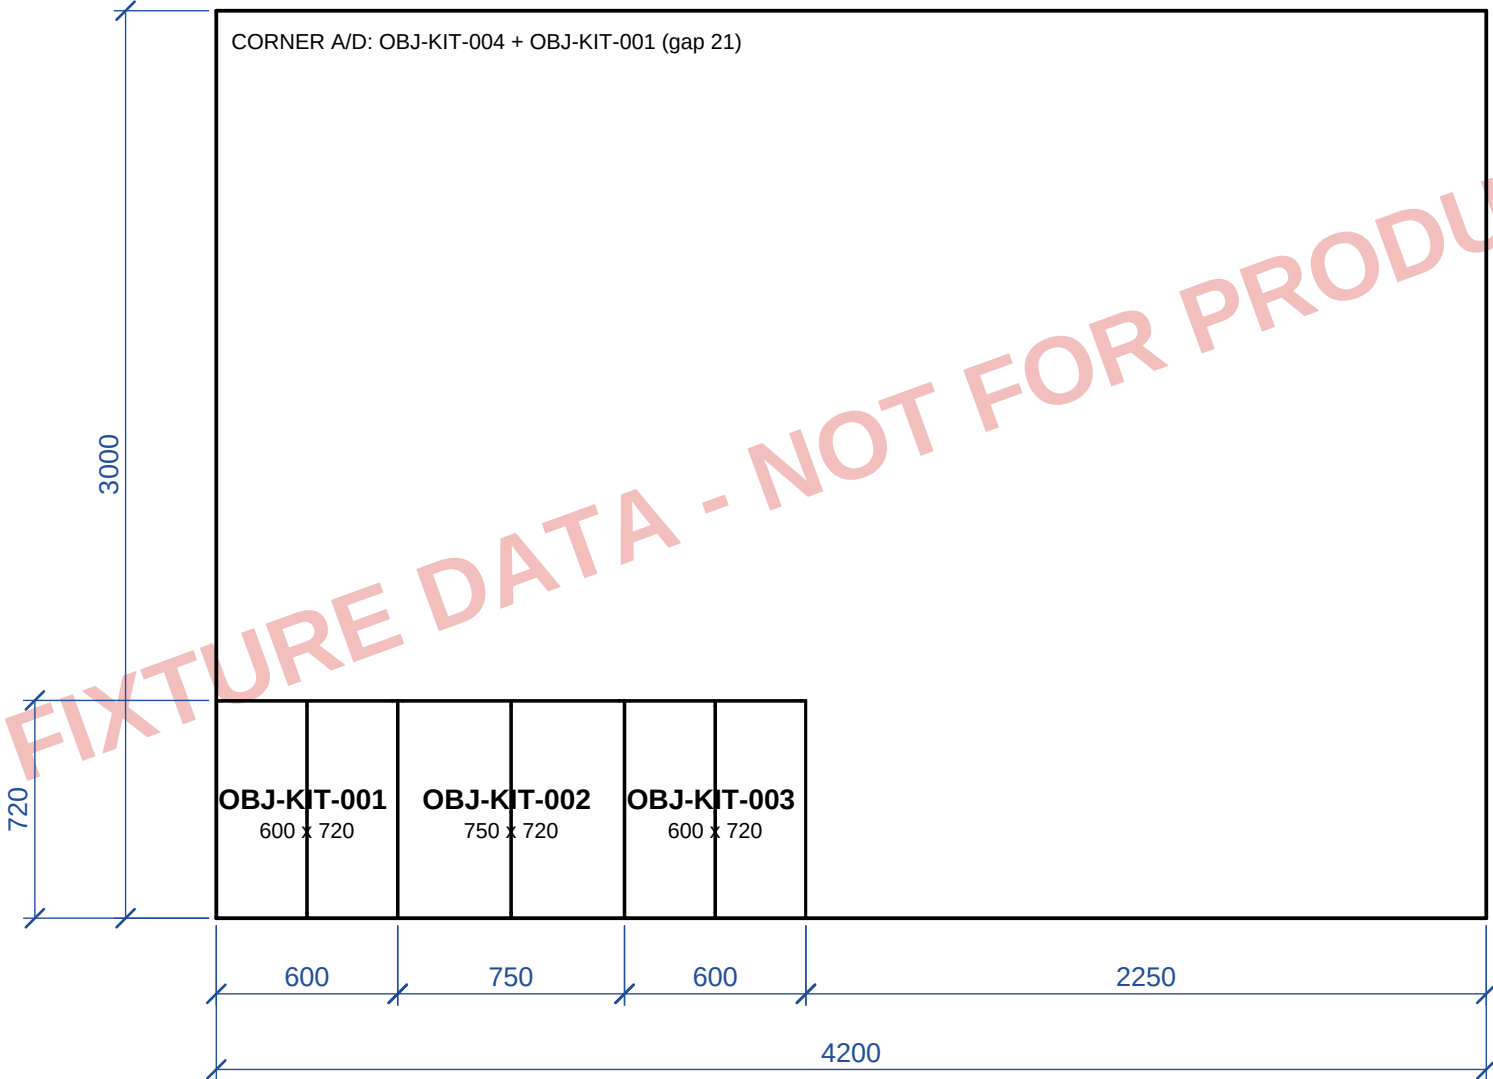


WALL A INTERNAL ELEVATION KITCHEN SCALE 1:25

NOTES

- 1. All dimensions in millimetres. Dimensions are read from the resolved room model, not measured from this drawing.
- 2. View from inside the room facing wall A; visible edges only. Objects on other walls are shown on their own wall elevations.
- 3. RUN:A:1: OBJ-KIT-001, OBJ-KIT-002, OBJ-KIT-003 (length 1950).
- 4. Adjacency: OBJ-KIT-001/OBJ-KIT-002 touching; OBJ-KIT-002/OBJ-KIT-003 touching.
- 5. Corner D/A: OBJ-KIT-004 + OBJ-KIT-001, gap 21.
- 6. Derived from design version dv_001; planning standard TEST_FIXTURE_PLANNING_STANDARD v0.0.1 (TEST_FIXTURE); 4 object(s).
- 7. TEST_FIXTURE data in use: construction standard TEST_FIXTURE_CONSTRUCTION_STANDARD; edge band standard TEST_FIXTURE_EDGE_BAND_STANDARD; hardware dataset HETTICH_TEST_FIXTURE; planning standard TEST_FIXTURE_PLANNING_STANDARD. Values are synthetic.
- 8. 34 validation BLOCKER(s) outstanding: this drawing must not be used for production.

PROJECT	LSA-BLR-2026-0001 (project_001)
ROOM	Kitchen
DRAWING TITLE	WALL A INTERNAL ELEVATION - KITCHEN
DRAWING NO. / SHEET	KIT-WE-A SHEET 1 OF 1
REVISION / DATE	A 2026-09-26
DESIGNER / CHECKER	TEST DESIGNER / UNASSIGNED
SCALE	1:25
APPROVAL STATUS	PRELIMINARY
SOURCE DESIGN VERSION	dv_001 (DRAFT)
MODEL FINGERPRINT	13a066ddbfd7f0
DATA CLASSIFICATION	TEST_FIXTURE

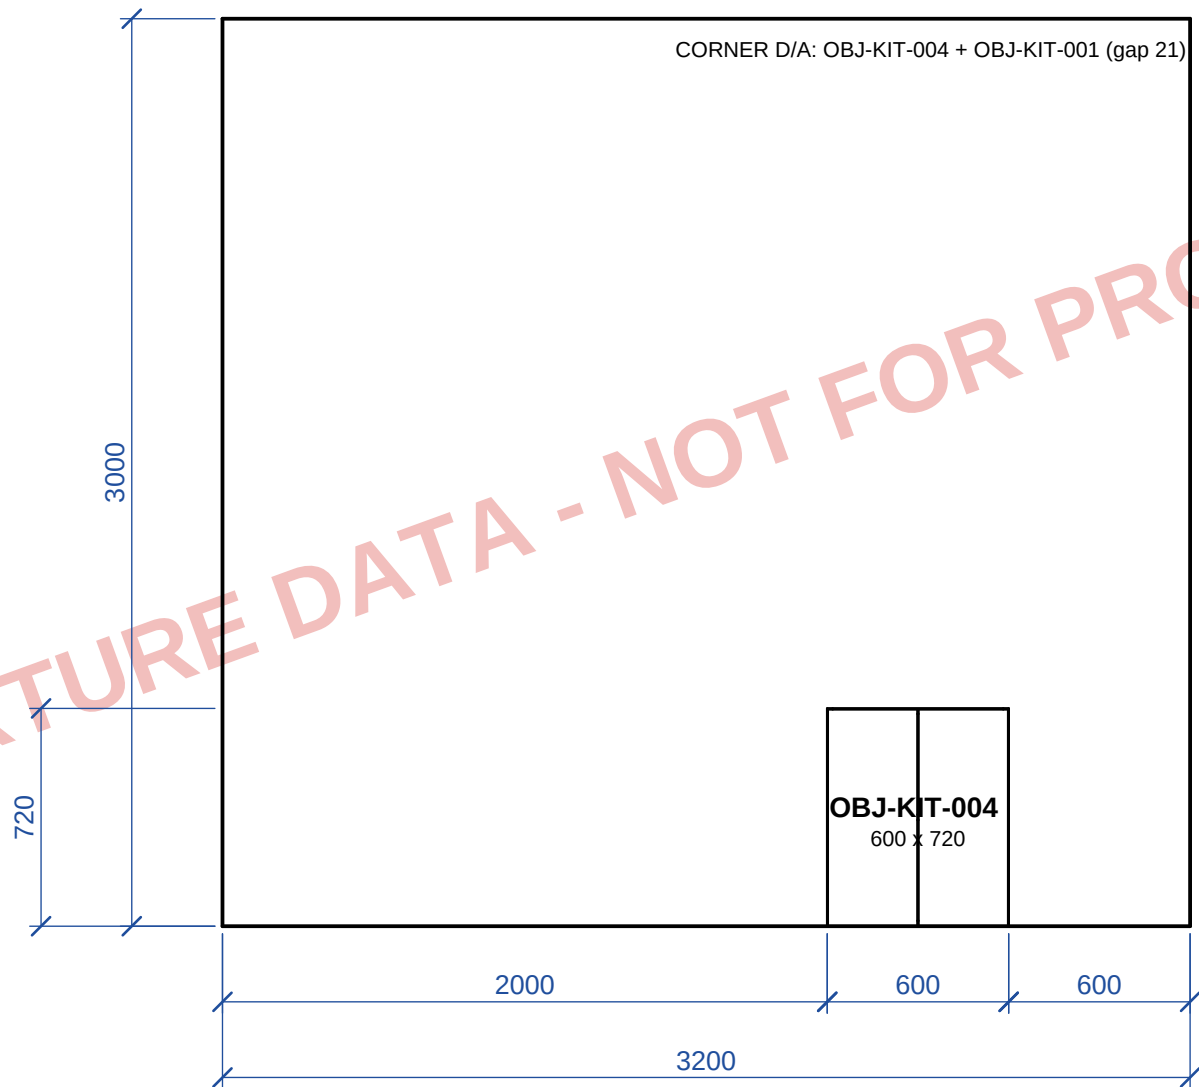

WALL D INTERNAL ELEVATION KITCHEN SCALE 1:25

NOTES

1. All dimensions in millimetres. Dimensions are read from the resolved room model, not measured from this drawing.
2. View from inside the room facing wall D; visible edges only. Objects on other walls are shown on their own wall elevations.
3. RUN:D:1: OBJ-KIT-004 (length 600).
4. Corner D/A: OBJ-KIT-004 + OBJ-KIT-001, gap 21.
5. Derived from design version dv_001; planning standard TEST_FIXTURE_PLANNING_STANDARD v0.0.1 (TEST_FIXTURE); 4 object(s).
6. TEST FIXTURE data in use: construction standard TEST_FIXTURE_CONSTRUCTION_STANDARD; edge band standard TEST_FIXTURE_EDGE_BAND_STANDARD; hardware dataset HETTICH_TEST_FIXTURE; planning standard TEST_FIXTURE_PLANNING_STANDARD. Values are synthetic.
7. 34 validation BLOCKER(s) outstanding: this drawing must not be used for production.

PROJECT	LSA-BLR-2026-0001 (project_001)
ROOM	Kitchen
DRAWING TITLE	WALL D INTERNAL ELEVATION - KITCHEN
DRAWING NO. / SHEET	KIT-WE-D SHEET 1 OF 1
REVISION / DATE	A 2026-09-26
DESIGNER / CHECKER	TEST DESIGNER / UNASSIGNED
SCALE	1:25
APPROVAL STATUS	PRELIMINARY
SOURCE DESIGN VERSION	dv_001 (DRAFT)
MODEL FINGERPRINT	13a066ddbdf7f0
DATA CLASSIFICATION	TEST_FIXTURE

ROOM PANEL SCHEDULE KITCHEN

NO	COMPONENT ID	TYPE	W	H	T	MATERIAL	GRAIN	EDGE BANDING	FINISH	QTY	STATUS
	OBJ-KIT-001	KIT_BASE_STANDARD	600	720	560			WALL A @ 0			OBJECT
1	OBJ-KIT-001-SL	SIDE_LEFT	560	720	18	BOARD_BWP_18	HEIGHT	EDGE_ABS_0_8MM (F)	-	1	GENERATED
2	OBJ-KIT-001-SR	SIDE_RIGHT	560	720	18	BOARD_BWP_18	HEIGHT	EDGE_ABS_0_8MM (F)	-	1	GENERATED
3	OBJ-KIT-001-BOT	BOTTOM	564	560	18	BOARD_BWP_18	WIDTH	EDGE_ABS_0_8MM (F)	-	1	GENERATED
4	OBJ-KIT-001-TSF	TOP_SUPPORT_FRONT	564	100	18	BOARD_BWP_18	WIDTH	EDGE_ABS_0_8MM (F)	-	1	GENERATED
5	OBJ-KIT-001-TSB	TOP_SUPPORT_BACK	564	100	18	BOARD_BWP_18	WIDTH	NONE	-	1	GENERATED
6	OBJ-KIT-001-BCK	BACK	580	710	6	BOARD_BACK_6	NONE	NONE	-	1	GENERATED
7	OBJ-KIT-001-SHF-01	SHELF	562	518	18	BOARD_BWP_18	WIDTH	EDGE_ABS_0_8MM (F)		1	GENERATED
8	OBJ-KIT-001-SHT-L	SHUTTER	297	717	18	BOARD_HDHMR_18	HEIGHT	EDGE_ABS_2MM (T/BT/L/R)	LAMINATE_WHITE x2	1	GENERATED
9	OBJ-KIT-001-SHT-R	SHUTTER	297	717	18	BOARD_HDHMR_18	HEIGHT	EDGE_ABS_2MM (T/BT/L/R)	LAMINATE_WHITE x2	1	GENERATED
	OBJ-KIT-002	KIT_BASE_STANDARD	750	720	560			WALL A @ 600			OBJECT
10	OBJ-KIT-002-SL	SIDE_LEFT	560	720	18	BOARD_BWP_18	HEIGHT	EDGE_ABS_0_8MM (F)	-	1	GENERATED
11	OBJ-KIT-002-SR	SIDE_RIGHT	560	720	18	BOARD_BWP_18	HEIGHT	EDGE_ABS_0_8MM (F)	-	1	GENERATED
12	OBJ-KIT-002-BOT	BOTTOM	714	560	18	BOARD_BWP_18	WIDTH	EDGE_ABS_0_8MM (F)	-	1	GENERATED
13	OBJ-KIT-002-TSF	TOP_SUPPORT_FRONT	714	100	18	BOARD_BWP_18	WIDTH	EDGE_ABS_0_8MM (F)	-	1	GENERATED
14	OBJ-KIT-002-TSB	TOP_SUPPORT_BACK	714	100	18	BOARD_BWP_18	WIDTH	NONE	-	1	GENERATED
15	OBJ-KIT-002-BCK	BACK	730	710	6	BOARD_BACK_6	NONE	NONE	-	1	GENERATED
16	OBJ-KIT-002-SHF-01	SHELF	712	518	18	BOARD_BWP_18	WIDTH	EDGE_ABS_0_8MM (F)	-	1	GENERATED
17	OBJ-KIT-002-SHT-L	SHUTTER	372	717	18	BOARD_HDHMR_18	HEIGHT	EDGE_ABS_2MM (T/BT/L/R)	LAMINATE_WHITE x2	1	GENERATED
18	OBJ-KIT-002-SHT-R	SHUTTER	372	717	18	BOARD_HDHMR_18	HEIGHT	EDGE_ABS_2MM (T/BT/L/R)	LAMINATE_WHITE x2	1	GENERATED
	OBJ-KIT-003	KIT_BASE_STANDARD	600	720	560			WALL A @ 1350			OBJECT
19	OBJ-KIT-003-SL	SIDE_LEFT	560	720	18	BOARD_BWP_18	HEIGHT	EDGE_ABS_0_8MM (F)	-	1	GENERATED
20	OBJ-KIT-003-SR	SIDE_RIGHT	560	720	18	BOARD_BWP_18	HEIGHT	EDGE_ABS_0_8MM (F)	-	1	GENERATED
21	OBJ-KIT-003-BOT	BOTTOM	564	560	18	BOARD_BWP_18	WIDTH	EDGE_ABS_0_8MM (F)	-	1	GENERATED
22	OBJ-KIT-003-TSF	TOP_SUPPORT_FRONT	564	100	18	BOARD_BWP_18	WIDTH	EDGE_ABS_0_8MM (F)	-	1	GENERATED
23	OBJ-KIT-003-TSB	TOP_SUPPORT_BACK	564	100	18	BOARD_BWP_18	WIDTH	NONE	-	1	GENERATED

NOTES

1. All dimensions in millimetres. Dimensions are read from the resolved room model, not measured from this drawing.
2. Edge codes: F front, BK back, T top, BT bottom, L left, R right. Rows grouped by object.
3. Derived from design version dv_001; planning standard TEST_FIXTURE_PLANNING_STANDARD v0.0.1 (TEST_FIXTURE); 4 object(s).
4. TEST FIXTURE data in use: construction standard TEST_FIXTURE_CONSTRUCTION_STANDARD; edge band standard TEST_FIXTURE_EDGE_BAND_STANDARD; hardware dataset HETTICH_TEST_FIXTURE; planning standard TEST_FIXTURE_PLANNING_STANDARD.
Values are synthetic.
5. 34 validation BLOCKER(s) outstanding: this drawing must not be used for production.

PROJECT	LSA-BLR-2026-0001 (project_001)
ROOM	Kitchen
DRAWING TITLE	ROOM PANEL SCHEDULE - KITCHEN
DRAWING NO. / SHEET	KIT-RPS-001 SHEET 1 OF 2
REVISION / DATE	A 2026-09-26
DESIGNER / CHECKER	TEST DESIGNER / UNASSIGNED
SCALE	NTS
APPROVAL STATUS	PRELIMINARY
SOURCE DESIGN VERSION	dv_001 (DRAFT)
MODEL FINGERPRINT	13a066ddbfd7f0
DATA CLASSIFICATION	TEST_FIXTURE

ROOM PANEL SCHEDULE KITCHEN

NO	COMPONENT ID	TYPE	W	H	T	MATERIAL	GRAIN	EDGE BANDING	FINISH	QTY	STATUS
24	OBJ-KIT-003-BCK	BACK	580	710	6	BOARD_BACK_6	NONE	NONE	-	1	GENERATED
25	OBJ-KIT-003-SHF-01	SHELF	562	518	18	BOARD_BWP_18	WIDTH	EDGE_ABS_0_8MM (F)	-	1	GENERATED
26	OBJ-KIT-003-SHT-L	SHUTTER	297	717	18	BOARD_HDHMR_18	HEIGHT	EDGE_ABS_2MM (T/BT/L/R)	LAMINATE_WHITE x2	1	GENERATED
27	OBJ-KIT-003-SHT-R	SHUTTER	297	717	18	BOARD_HDHMR_18	HEIGHT	EDGE_ABS_2MM (T/BT/L/R)	LAMINATE_WHITE x2	1	GENERATED
	OBJ-KIT-004	KIT_BASE_STANDARD	600	720	560			WALL D @ 2000			OBJECT
28	OBJ-KIT-004-SL	SIDE_LEFT	560	720	18	BOARD_BWP_18	HEIGHT	EDGE_ABS_0_8MM (F)	-	1	GENERATED
29	OBJ-KIT-004-SR	SIDE_RIGHT	560	720	18	BOARD_BWP_18	HEIGHT	EDGE_ABS_0_8MM (F)	-	1	GENERATED
30	OBJ-KIT-004-BOT	BOTTOM	564	560	18	BOARD_BWP_18	WIDTH	EDGE_ABS_0_8MM (F)		1	GENERATED
31	OBJ-KIT-004-TSF	TOP_SUPPORT_FRONT	564	100	18	BOARD_BWP_18	WIDTH	EDGE_ABS_0_8MM (F)		1	GENERATED
32	OBJ-KIT-004-TSB	TOP_SUPPORT_BACK	564	100	18	BOARD_BWP_18	WIDTH	NONE	-	1	GENERATED
33	OBJ-KIT-004-BCK	BACK	580	710	6	BOARD_BACK_6	NONE	NONE	-	1	GENERATED
34	OBJ-KIT-004-SHF-01	SHELF	562	518	18	BOARD_BWP_18	WIDTH	EDGE_ABS_0_8MM (F)	-	1	GENERATED
35	OBJ-KIT-004-SHT-L	SHUTTER	297	717	18	BOARD_HDHMR_18	HEIGHT	EDGE_ABS_2MM (T/BT/L/R)	LAMINATE_WHITE x2	1	GENERATED
36	OBJ-KIT-004-SHT-R	SHUTTER	297	717	18	BOARD_HDHMR_18	HEIGHT	EDGE_ABS_2MM (T/BT/L/R)	LAMINATE_WHITE x2	1	GENERATED

NOTES

1. All dimensions in millimetres. Dimensions are read from the resolved room model, not measured from this drawing.
2. Edge codes: F front, BK back, T top, BT bottom, L left, R right. Rows grouped by object.
3. Derived from design version dv_001; planning standard TEST_FIXTURE_PLANNING_STANDARD v0.0.1 (TEST_FIXTURE); 4 object(s).
4. TEST FIXTURE data in use: construction standard TEST_FIXTURE_CONSTRUCTION_STANDARD; edge band standard TEST_FIXTURE_EDGE_BAND_STANDARD; hardware dataset HETTICH_TEST_FIXTURE; planning standard TEST_FIXTURE_PLANNING_STANDARD.
Values are synthetic.
5. 34 validation BLOCKER(s) outstanding: this drawing must not be used for production.

PROJECT	LSA-BLR-2026-0001 (project_001)
ROOM	Kitchen
DRAWING TITLE	ROOM PANEL SCHEDULE - KITCHEN
DRAWING NO. / SHEET	KIT-RPS-001 SHEET 2 OF 2
REVISION / DATE	A 2026-09-26
DESIGNER / CHECKER	TEST DESIGNER / UNASSIGNED
SCALE	NTS
APPROVAL STATUS	PRELIMINARY
SOURCE DESIGN VERSION	dv_001 (DRAFT)
MODEL FINGERPRINT	13a066ddbdf7f0
DATA CLASSIFICATION	TEST_FIXTURE